



A COMMUNITY OF CHOICE

Planning and Development Department

2101 O'Neil Avenue, Suite 202, Cheyenne WY 82001
(Phone) 307-637-6282 (Fax) 307-637-6366

MEMO

To: Honorable Mayor Patrick Collins and Members of the City Council
From: Seth Lloyd, Planner
Subject: UDC-22-00025 – Olivet Cemetery, 4th Filing Final Plat
Date: March 14, 2022

Background:

The item for consideration is a *Final Plat*. This is approved by Resolution.

The proposed Governing Body review schedule is as follows:

- Introduction and Referral 3/14/2022
- Public Services Committee 3/22/2022
- Final consideration 3/28/2022

Planning Commission Recommendation:

The Planning Commission heard this item at their March 7, 2022 meeting and recommended the Governing Body approve this application by a vote of 4-0.

The Planning Commission Staff report is attached and has not been changed.

Attachments:

1. Resolution
2. Planning Commission Staff Report

RESOLUTION NO. _____

ENTITLED: "A RESOLUTION AUTHORIZING THE MAYOR AND THE CITY CLERK TO SIGN A FINAL PLAT FOR OLIVET CEMETERY, 4TH FILING, A REPLAT OF A PORTION OF OLIVET CEMETERY, 3RD FILING AND A PLAT OF A PORTION OF THE SOUTHEAST QUARTER OF THE SOUTHEAST QUARTER OF SECTION 30, TOWNSHIP 14 NORTH, RANGE 66 WEST, OF THE 6TH P.M., CHEYENNE, LARAMIE COUNTY, WYOMING (LOCATED NORTHWEST OF THE INTERSECTION OF PERSHING BOULEVARD AND AIRPORT PARKWAY)."

WHEREAS, Church of Saint Mary, has subdivided said land in accordance with the statutes in such cases made and provided; and

WHEREAS, Church of Saint Mary, the owners of the above described land, has caused a subdivision plat of said land to be made, acknowledged, and certified, particularly describing the lots, block, easements, and right-of-way; and

WHEREAS, the above described subdivision plat has been presented to the City of Cheyenne Planning Commission for consideration; the Planning Commission has recommended that said plat be approved by the Governing Body; and the plat has been duly executed by the Development Office; and

NOW, THEREFORE BE IT RESOLVED BY THE GOVERNING BODY OF THE CITY OF CHEYENNE, WYOMING, THAT the subdivision described as Olivet Cemetery, 4th Filing, Cheyenne, Wyoming, be and the same hereby is approved and confirmed as presented, and that the Mayor and the City Clerk be and are hereby authorized, empowered, and directed to execute said plat.

PRESENTED, READ AND ADOPTED THIS _____ DAY OF _____, 2022.

PATRICK COLLINS, MAYOR

(SEAL)
ATTEST:

KRISTINA F. JONES, CITY CLERK



A COMMUNITY OF CHOICE

Planning and Development Department

2101 O'Neil Avenue, Suite 202, Cheyenne WY 82001

(Phone) 307-637-6282 (Fax) 307-637-6366

CITY OF CHEYENNE PLANNING COMMISSION

MARCH 7, 2022

STAFF REPORT

FILE: UDC-22-00025: Olivet Cemetery, 4th Filing (Expedited Review)

REQUEST: A plat proposing platting cemetery plots.

LOCATION: Northwest of the intersection of Pershing and Airport Parkway.


APPLICANT: Casey Palma – Steil Surveying Services

OWNER: St. Mary's Church

ZONING: P Public

PURPOSE: A plat of previously undivided land, and a replat of previously divided land, to create and restructure cemetery plots.

PREPARED BY: Seth Lloyd, Planner II

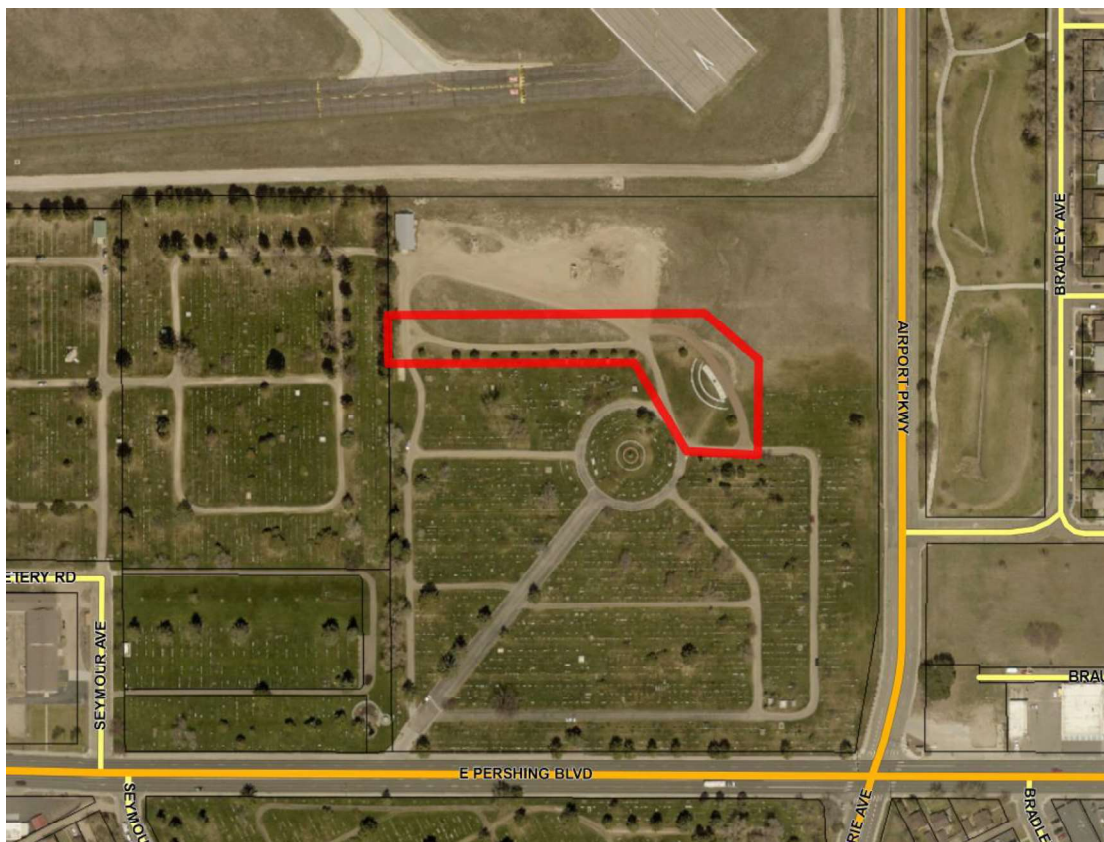

RECOMMENDED MOTION:

Move to recommend **approval** of Olivet Cemetery, 4th Filing, advancing the Final Plat to the Governing Body, with the following conditions:

1. Update the map to reflect the status as a final plat approved by the governing body (instead of an administrative plat).
2. Update the map to remove references to "Mount Olivet Cemetery".

APPLICABLE CITY CODE SECTION(S) AND PLANS:

- UDC 2.1.2 Preliminary Plat Approval
- UDC Article 4 Subdivisions
- UDC Article 5 Zoning Regulations
- PlanCheyenne

BACKGROUND:

The applicant is requesting approval of a plat for approximately 1.5 acres of land to create cemetery plots. While the division of a cemetery into plots is not a typical subdivision, all other cemetery divisions of record have been approved by the Governing Body, including Lakeview, Bethel, IOOF, and the previous portions of Olivet located south of this proposed plat. The original Olivet division and the Jewish cemetery division were not readily available in the various record repositories.

Areas previously platted are eligible for a "Revised Final Plat" under the Administrative Plat regulations of the UDC; however, as no documents were able to be obtained indicating what (if any) division of Olivet north of the current 3rd Filing occurred, City Staff has determined this proposed plat requires Governing Body approval.

The City has a cemetery layout for all cemeteries located in this area of the community, and the area north of third filing is blank. Various repositories were investigated by Staff and the applicant and, as of this writing, no previous plat has been found. Should the previous document be found, this plat may be withdrawn and the procedures guiding administrative plats may be followed.

SURROUNDING LAND USE AND ZONING:

	Future Land Use Designation	Zoning	Land Use
Subject Site	Public and Quasi-public	P Public	Cemetery and vacant
North	Public and Quasi-public	P	Vacant (Cemetery-owned)
South	Public and Quasi-public	P	Cemetery
East	Public and Quasi-public	P	Cemetery and vacant
West	Public and Quasi-public	P	Cemetery

ANALYSIS OF APPLICATION CONFORMANCE WITH REVIEW CRITERIA:

Should the Planning Commission wish to recommend approval of the plat, the Commission must make the following findings required in UDC 2.1.2.d – a detailed analysis is below. **NOTE – as a cemetery, not all review criteria are as strictly applicable to this application.**

- 1) **The application is in accordance with the development policies and physical patterns identified in the Comprehensive Plan. (UDC 2.1.2.d.1)**

This development is in conformance with the principles and future land uses identified in PlanCheyenne. The property is within the Urban Service Boundary and has access to all utilities.

The future land use map within PlanCheyenne designates this area (and all surrounding property) as Public and Quasi-public. Cemeteries are given as an example quasi-public use.

The application **complies** with this review criterion.

- 2) The application reflects sound planning and urban design principles with respect to existing and potential future development in the vicinity, including consideration of current and future streets, open spaces, blocks and lots, and public utilities or facilities. (UDC 2.1.2.d.2)**

This cemetery layout provides reasonable access to all plots and is similar in nature to surrounding cemeteries. Urban design principles are largely not applicable to cemeteries, and the over-arching parcel (as an open space) is an important part of a community's fabric.

The application **complies** with this review criterion, to the extent the criterion is applicable.

- 3) The division of land meets the purposes, intent, and all applicable standards in Article 4. (UDC 2.1.2.d.3)**

Transportation Network:

The plat proposes dividing an area already owned for cemetery use. The over-arching parcel is part of an extra-large block (containing the airport), and connections could be provided through the over-arching property. A Greenway connection (linking Airport Parkway and Evans Avenue) is proposed in the vicinity, but outside the boundaries of the proposed plat.

Community Facility Fees:

Due to the public and open-space like nature of a cemetery, this plat is exempt from plat fees.

Open Space:

As a cemetery, this plat is largely entirely open space in nature.

Required Improvements:

While a form of land division, it is not anticipated that individual cemetery plots would require the same level of service as typical developable parcels. Utilities and access are available to the over-arching development. No re-alignment of utilities or easements are necessary.

The application **complies** with this review criterion, to the extent the criterion is applicable.

- 4) Any phasing proposed in the application is clearly indicated and demonstrates a logical and well-planned development pattern. This may include consideration of amenities and public facilities of the subdivision within each phase compared to the anticipated timing or the likelihood of future phases being constructed as planned. (UDC 2.1.2.d.4)**

This plat represents one phase of the cemetery – roughly the next 'step' northward. No specific phasing is proposed within this plat.

The application **complies** with this review criterion.

- 5) **The impacts identified in specific studies or technical reports that were prepared or requested to be prepared in association with the application, and whether the findings and recommendations of these reports, or any modifications or conditions on approval of the application, can mitigate these impacts. (UDC 2.1.2.d.5)**

No technical studies were requested or provided in conjunction with this platting action. Generally, the subject property with the proposed use will have a negligible impact on traffic and drainage.

This review criterion is largely **not applicable** to this application.

- 6) **Lots proposed for development shall be buildable lots according to the existing or proposed zoning district standards, result in design and development patterns that meet the Intent and Applicability statements of the existing or proposed zoning district, and not aggravate nonconforming setbacks or currently adopted building and fire code access and separation requirements. (UDC 2.1.2.d.6)**

The proposed plat is to allow individual plots to be laid out in an over-arching cemetery parcel. The over-arching parcel meets the anticipated development pattern of the P zone.

This review criterion is largely **not applicable** to this application.

- 7) **All parcels not proposed as buildable lots and which are not dedicated to and accepted by the City shall have a clearly defined entity responsible for ongoing maintenance. (UDC 2.1.2.d.7)**

All plots are generally 'unbuildable' from a typical development standpoint. The over-arching ownership and maintenance patterns are not anticipated to be modified with this platting action.

The application **complies** with this review criterion, to the extent the criterion is applicable.

- 8) **The application will not create any undue influence on existing or potential development for adjacent property considering the existing zoning and Comprehensive Plan policies for that property. (UDC 2.1.2.d.8)**

The surrounding area to the south and west is previously developed with cemetery plots. The areas to the north and east are largely vacant, but are anticipated to develop with cemetery plots in the future. This action maintains connections to the previously divided areas, and leaves reasonable access to the future phases.

The application **complies** with this review criterion.

- 9) **The application is not harmful to the public health, safety, and welfare. (UDC 2.1.2.d.9)**

Staff is satisfied the proposed plat would not adversely affect the public health, safety, or general welfare.

The application **complies** with this review criterion.

- 10) Remainder lot(s) shall be clearly identified on the preliminary plat and shall not be developed or proposed for development for purposes. Remainder lot(s) shall be noted and described on all plats either graphically or by legal description. (UDC 2.1.2.d.10)**

Remainder lots are not proposed with this plat.

The application **complies** with this review criterion.

- 11) The layout and design of the final plat is in substantial compliance with the approved preliminary plat considering the number of lots or parcels, street and block layout, and access, and any deviations in the final plat brings the application in further compliance with the Comprehensive Plan. (UDC 2.1.3.d.1)**

The purposes behind the submittal and approval of a preliminary plat are largely not applicable to the division of cemetery plots.

This review criterion is largely **not applicable** to this application.

- 12) The application meets any conditions or modifications of the approved preliminary plat. (UDC 2.1.3.d.2)**

Conditions are technical in nature, and will be required to be addressed prior to recordation.

The application **complies** with this review criterion.

- 13) The application meets the purposes, intent, and applicable standards of Article 4. (UDC 2.1.3.d.3)**

As an expedited review, this Final Plat review criterion is covered by the equivalent Preliminary Plat review criterion (subsection 3 above).

The application **complies** with this review criterion.

CONFORMANCE WITH APPLICABLE PLANS:

The project is located in an area covered by the following plans:

- PlanCheyenne
- Pershing Boulevard Complete Streets
- Cheyenne Area On-Street Bicycle Plan and Greenway Plan Update

Conformance with PlanCheyenne is covered by review criterion 1. All other plans are largely silent on the development of this parcel, anticipating the property to be utilized as a cemetery. The proposed plat is in conformance with this expectation. The Cheyenne Area On-Street Bicycle Plan and Greenway Plan Update suggested a Greenway connection in this area (connecting Evans and Airport Parkway)

STAFF REVIEW:

Through the review process, comments were received regarding the following issues:

1. The location of a future Greenway connection in this area (north of the proposed plat).
2. Inability to find any documentation of a previous action dividing the northern portion of the property.

CONCLUSION:

This application meets all review criteria as filed.

ALTERNATIVES:

1. Recommend approval of the expedited preliminary plat, forwarding the Final Plat to the Governing Body.
2. Recommend approval of the preliminary plat with conditions and that a final plat addressing the conditions of approval be prepared and presented to the Governing Body (**Staff Recommendation**).
3. Recommend approval of the preliminary plat as submitted by the applicant and forward the preliminary plat to the Governing Body.
4. Recommend approval of the preliminary plat subject to staff's recommended conditions and forward the preliminary plat to the Governing Body.
5. Recommend denial of the preliminary plat based on findings of denial. The Planning Commission must conclude that the project does not meet all the review criteria. As part of the motion, findings for denial must be stated.
6. Postpone the project until issues identified during the meeting can be resolved.

General Information Regarding Alternatives:



The Planning Commission may modify staff's recommended conditions, delete conditions, add conditions, or decide contrary to staff's recommendation. In the event conditions are modified, the conditions shall relate to applicable review criteria. In the event that the Commission acts contrary to staff's recommendation or modifies conditions of approval, the Commission shall cite specific reasons (based on the review criteria) for approval or denial.

STAFF RECOMMENDATION:

Staff recommends approval of Olivet Cemetery, 4th Filing, advancing the Final Plat to the Governing Body.

ATTACHMENTS:

1. Zoning Map
2. Land Use Plan Map
3. Master Application Form
4. Plat

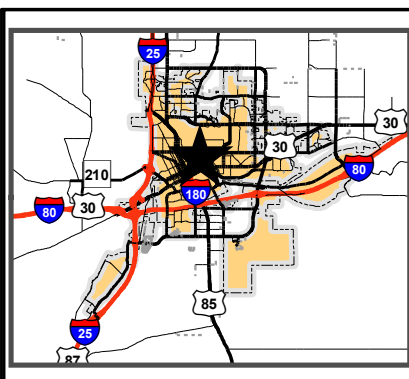
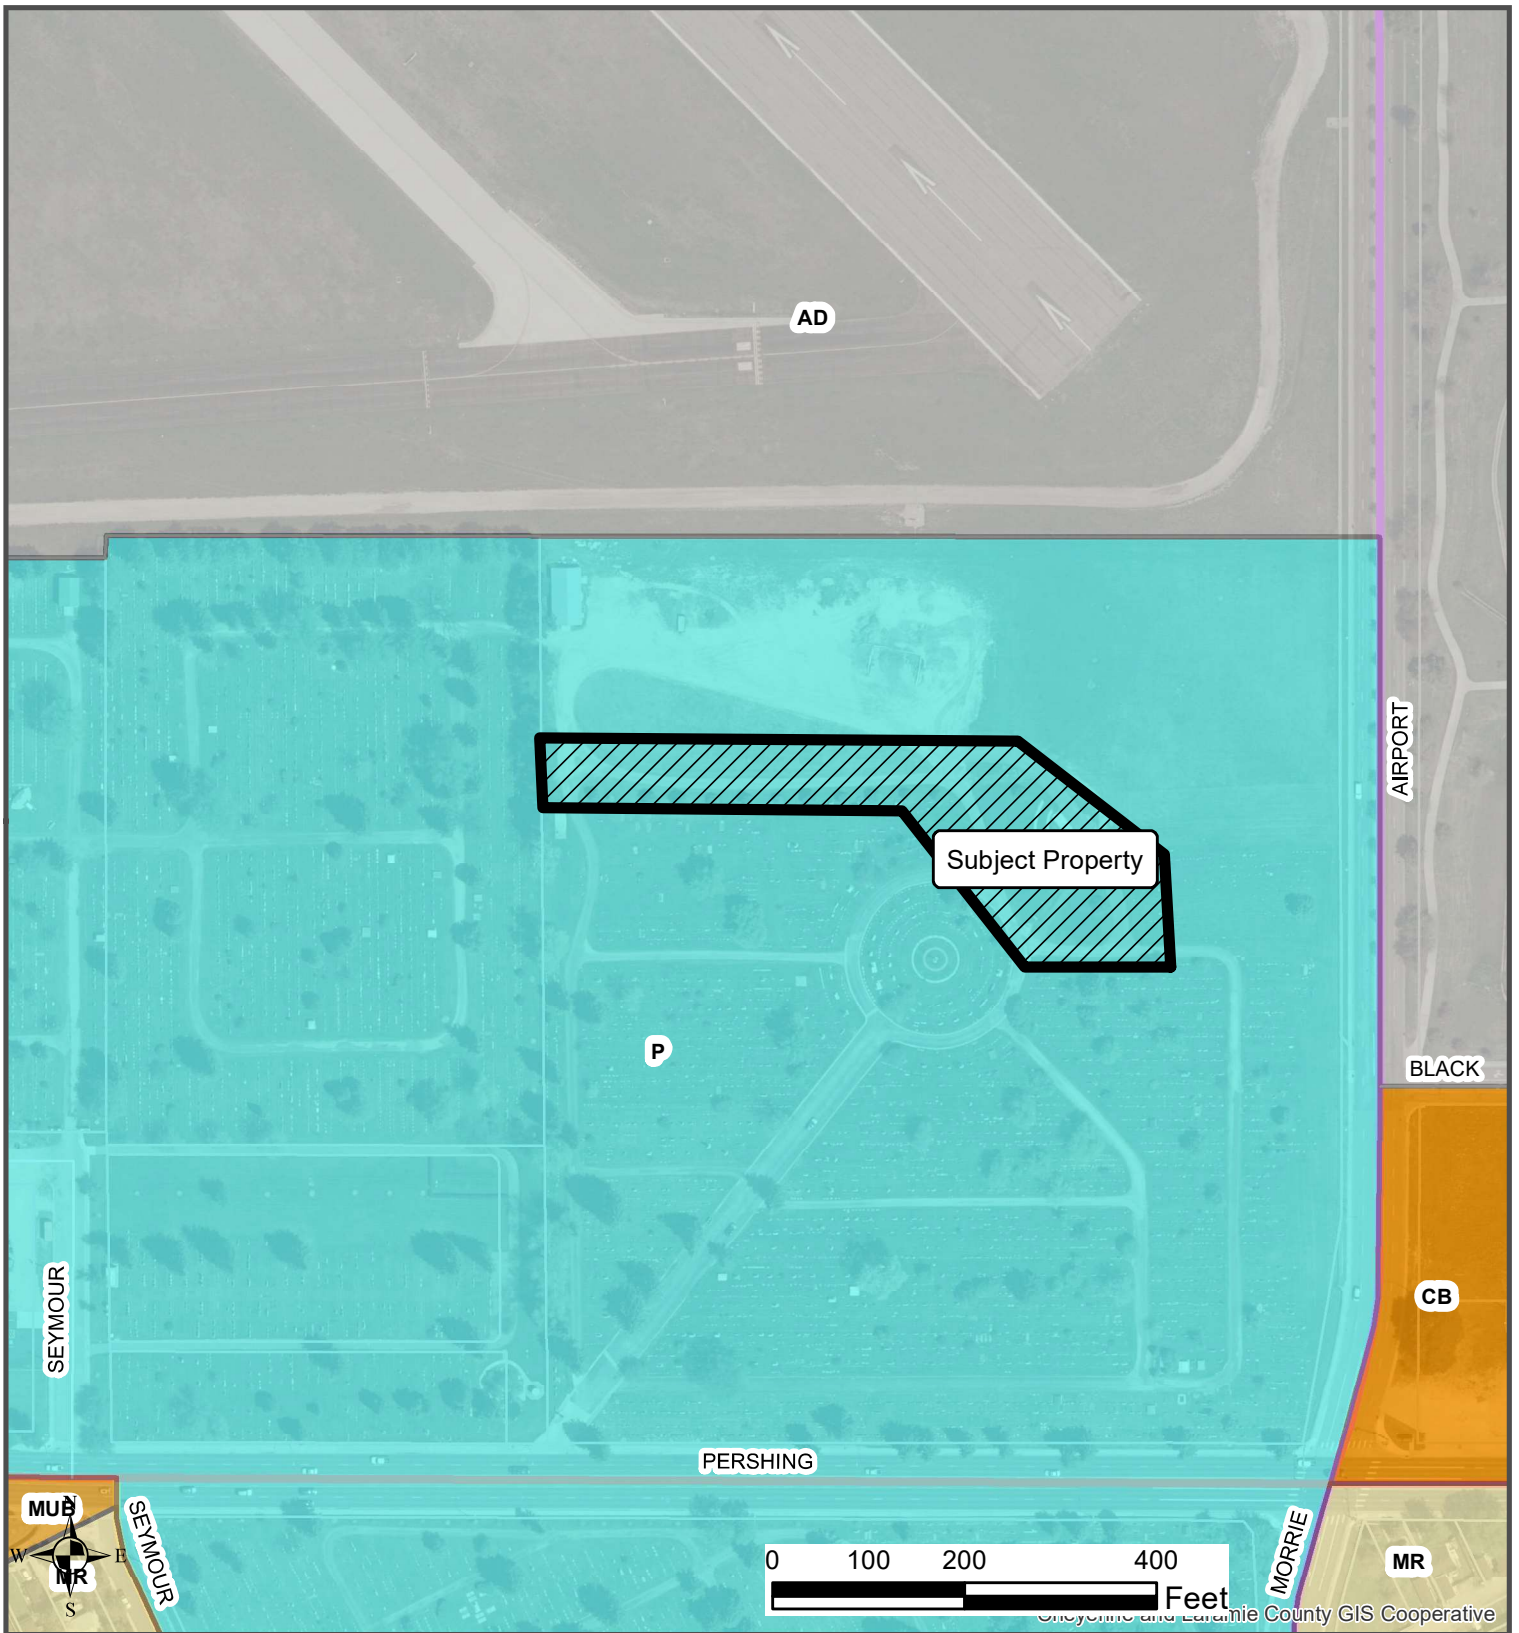


Attachment 1: Zoning Map UDC-22-00025

This map/data is made possible through the Cheyenne and Laramie County Cooperative GIS (CLCCGIS) Program and is for display purposes only. The CLCCGIS invokes its sovereign and governmental immunity in allowing access to or use of this data, makes no warranties as to the validity, and assumes no liability associated with the use or misuse of this information.

Legend

	Nov19_CityLimits		A-1 / Agricultural and Rural Residential
	Interstate		A-2 / Agricultural
	Principal Arterial		AG / City Agricultural
	Minor Arterial		MUR / Mixed Use Residential Emphasis
	Major Collector		CBD / Central Business District
	Minor Collector		CB / Community Business
	Local		NB / Neighborhood Business
	Private		MU / Mixed Use - County
	Platted not built		MUB / Mixed Use Business Emphasis
	HR / High Density Residential		MUE / Mixed Use Employment Emphasis
	MR / Medium Density Residential		HI / Heavy Industrial
	LR / Low Density Residential		LI / Light Industrial
	NR-2 / Neighborhood Residential - Med. Density		P / Public
	NR-3 / Neighborhood Residential - High Density		AD / Airport District
	AR / Agricultural Residential		PUD / Planned Unit Development
			X / Exempt

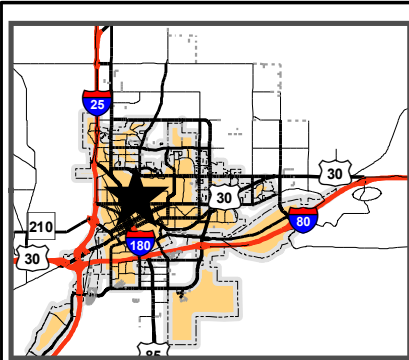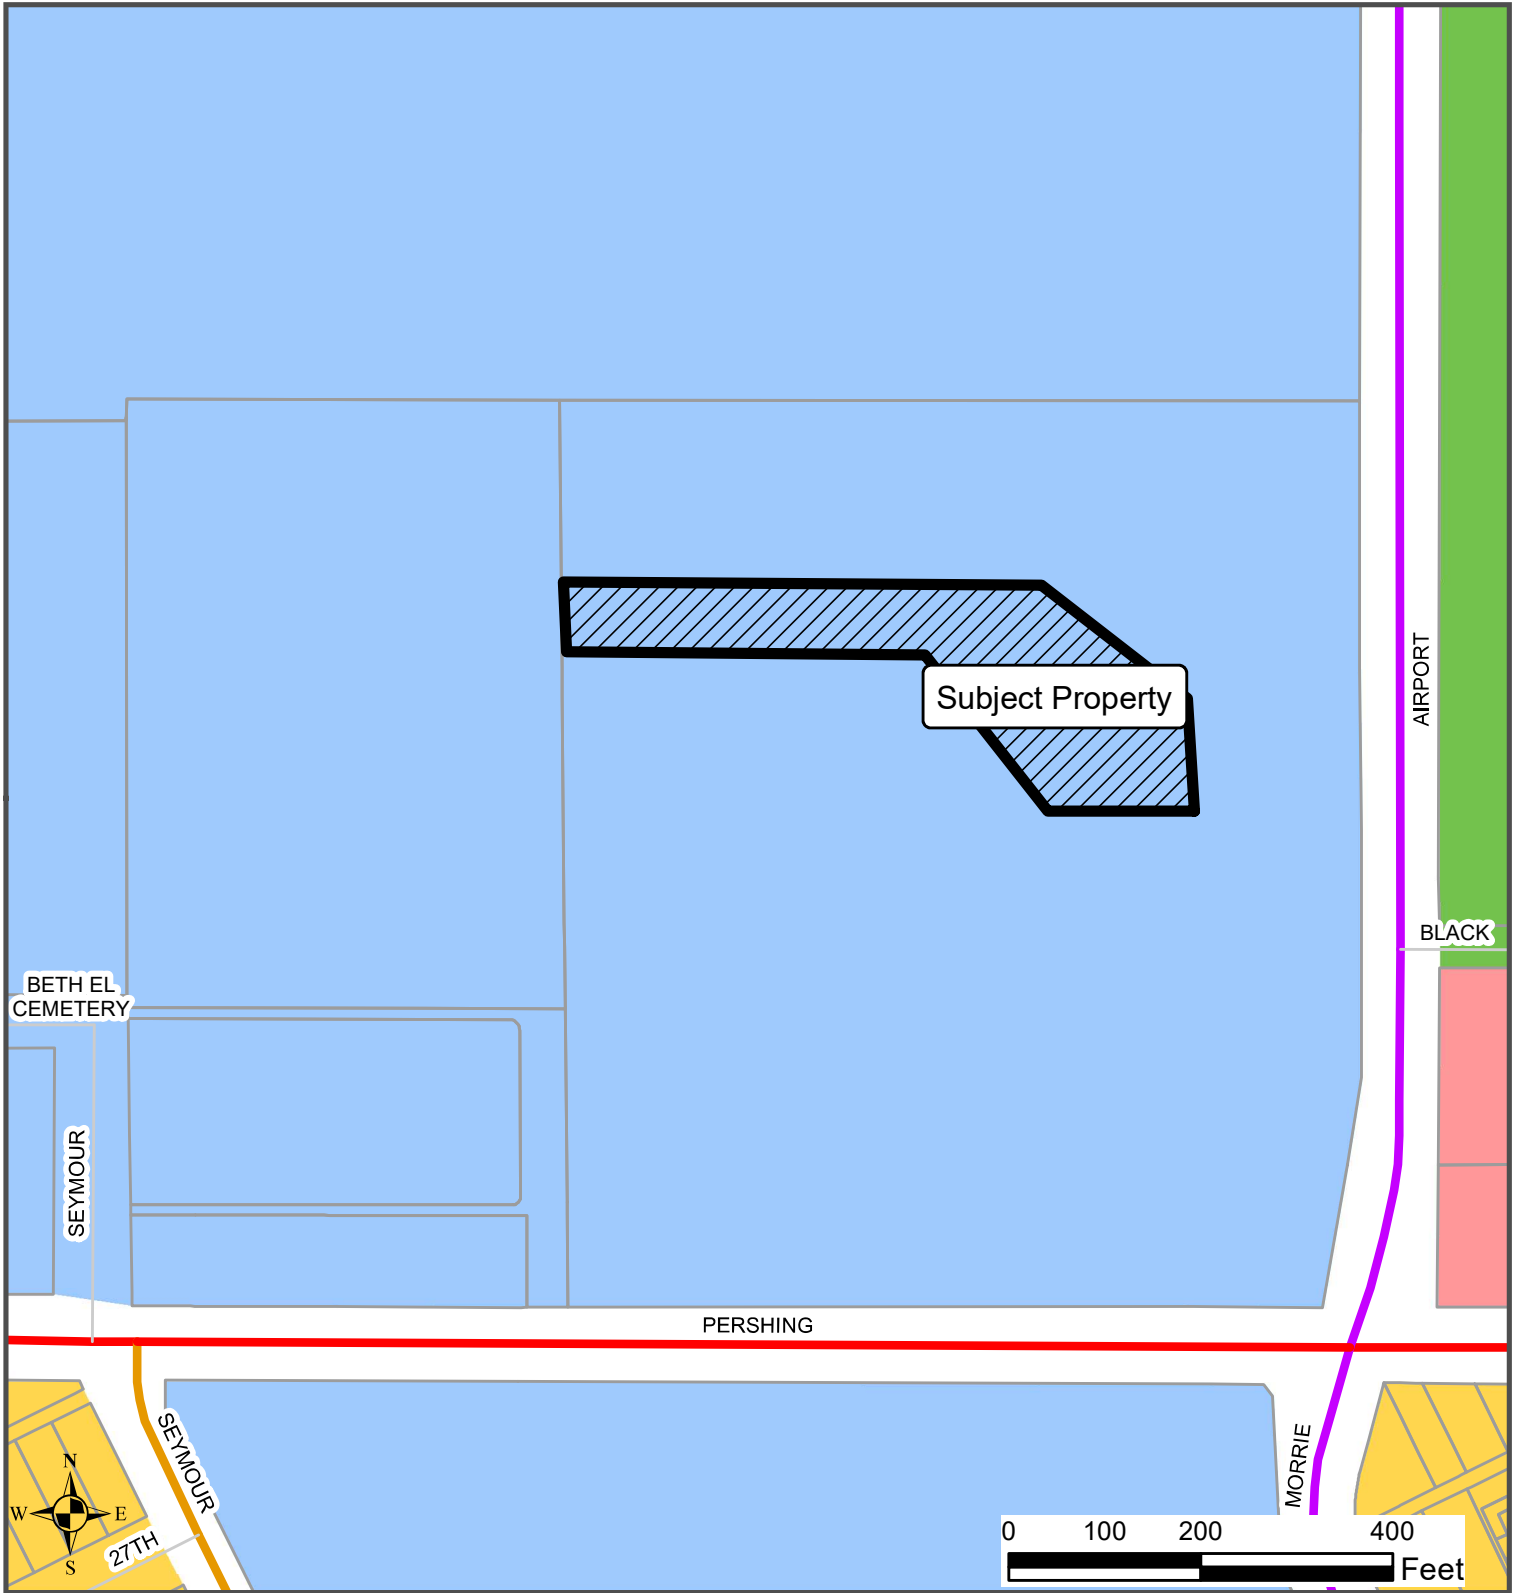

Attachment 2: Land Use Map UDC-22-00025

This map/data is made possible through the Cheyenne and Laramie County Cooperative GIS (CLCCGIS) Program and is for display purposes only. The CLCCGIS invokes its sovereign and governmental immunity in allowing access to or use of this data, makes no warranties as to the validity, and assumes no liability associated with the use or misuse of this information.

Legend

Nov19_CityLimits	Agricultural/Rural	Industrial
Interstate	Rural Residential	Central Business District
Principal Arterial	Urban Transition Residential	Community Business
Minor Arterial	Urban Residential	Public and Quasi-Public
Major Collector	Mixed-Use Residential	Military/Federal
Minor Collector	Mixed-Use Commercial	Open Space and Parks
Local	Mixed-Use Employment	
Platted not built		
Private		
Ownership		

Planning and Development: Plat - Administrative

Submission date: **28 January 2022, 2:01PM**
Receipt number: **28**
Related form version: **11**

General Information

Applicant Name: **Church of St Mary c/o Neill O'Donnell**

Applicant Address: **P.O. Box 1268**

Applicant City: **Cheyenne**

Applicant State: **WY**

Applicant Zip Code: **82003**

Applicant Phone: **(307) 287-3702**

Applicant Email: **nodonnell@stmarycathedral.com**

Representative Name: **Steil Surveying Services**

Representative Address: **1102 W 19th St**

Representative City: **Cheyenne**

Representative State: **WY**

Representative Zip Code: **82001**

Representative Phone: **(307) 634-7273**

Representative Email: **SHansen@SteilSurvey.com**

Owner Name: **Church of St Mary c/o Neill O'Donnell**

Owner Address: **P.O. Box 1268**

Owner City: **Cheyenne**

Owner State:	WY
Owner Zip Code:	82003
Owner Phone:	(307) 287-3702
Owner Email:	nodonnell@stmarycathedral.com
Who is the primary contact regarding this application?	Representative
Letter of Authorization	0026_001_LOA.pdf
Project Location (Street Address or General Location):	NW Corner of E Pershing Blvd & Airport Parkway
Assessor's Parcel ID number(s)	14663040500900
Total Project Area	76,052 sf
Existing Zoning	P - Public

Application-Specific Information

Written Statement	RESUBMITTAL - AMENDED Admin Plat Approval EXPIRED 2/4/2021. Project #: UDC-20-00019 THE PURPOSE OF THIS ADMINISTRATIVE REPLAT IS TO RECONFIGURE THE CEMETERY PLOTS (LOTS) TO CORRESPOND TO CONSTRUCTED COLUMBARIUM(S), CIRCULATION DRIVES, AND FUTURE PLOT CONFIGURATION(S); THE PLAT VACATES 463 EXISTING CEMETERY PLOTS (LOTS) AND CREATES 423 NEW LOTS AS FOLLOWS: 412 CEMETERY PLOTS, 1 TRACT FOR CIRCULATION/PARKING (TRACT 100), 4 BUFFER/RESERVE TRACTS (TRACTS 500, 600, 700, 800), 4 OPEN SPACE TRACTS (TRACTS 200, 300, 400, 900), AND 2 UNDIVIDED BLOCKS FOR FUTURE INFILL (BLOCKS 15 & 16).
Current Subdivision	A PORTION OF MOUNT OLIVET CEMETERY & OLIVET CEMETERY 3rd FILING

Lots affected by this proposal

A PORTION OF MOUNT OLIVET CEMETERY AND ALL OF R1/C13, R2/C13, R3/C13, & R4/C13; BLOCK 4, AND LOTS A & E, R7/C12, BLOCK 4, OLIVET CEMETERY 3rd FILING AND ALL OF LOTS A, B, C, H, G, & F, R5/C13, BLOCK 4, AND LOTS A & F, R6/C13, BLOCK 4, OLIVET CEMETERY 3rd FILING AND ALL OF R7/C13, BLOCK 4, OLIVET CEMETERY 3rd FILING AND ALL OF BLOCK 7, INCLUSIVE, OLIVET CEMETERY; 3rd FILING CITY OF CHEYENNE, LARAMIE COUNTY, WYOMING

A pre-application meeting is required. Please indicate the date the pre-application meeting was held. **10/07/2020**

Upload any pre-application meeting notes or summaries relevant to this proposal. [LPafford_RE Olivet Cemetery, 4th Filing.pdf](#)
[pre-app mtg notes .pdf](#)

Are any easements proposed to be added, modified, or removed? **No**

If easements are proposed to be added, modified, or removed. Attach Franchise Utility approval letters from all affected utilities. Failure to provide this information could result in delay of application review.

Drainage Worksheet / Study [SSS19086_Admin Plat Drainage Waiver Req.pdf](#)

Transportation Worksheet / Study [SSS19086_Admin Plat Traffic Waiver Req.pdf](#)

Transportation Network Plan

Administrative Plat Drawing [SSS19089_OlivetCemetary-4thFiling-ALL_012822.pdf](#)

Signature / Certification

Applicant Signature

Name of signatory: Casey L Palma

A handwritten signature in black ink, appearing to read 'Casey L Palma', with a long horizontal line extending to the right.

[Uploaded signature image: CPalma_121218.png](#)

Please enter an email address for an email receipt.


CPalma@SteilSurvey.com

- DOMESTIC WATER & SANITARY SEWER PROVIDED BY CITY OF CHEYENNE BOPU - FIRE PROTECTION TO BE PROVIDED BY CHEYENNE FIRE & RESCUE - THE SURFACE ESTATE OF THE LAND TO BE SUBDIVIDED IS SUBJECT TO FULL AND EFFECTIVE DEVELOPMENT OF THE MINERAL ESTATE -

CURVE TABLE - BOUNDARY			
CURVE #	DELTA	CHORD LENGTH	ARC LENGTH
1	10° 00' 00"	10.000'	10.472'
2	20° 00' 00"	20.000'	20.944'
3	30° 00' 00"	30.000'	31.416'


LEGEND

- SET 1/2" ALUMINUM CAP ON 1/2" x 4" REBAR
 - FOUND 1/2" ALUMINUM CAP STAMPED
 - FOUND 1/2" REBAR
 - FOUND 1/2" REBAR IN MONUMENT
 - FOUND CHISEL "X"
 - FOUND PLASTIC CAP STAMPED "3 3/4"
- "THIRTY" DENOTES CHORD LENGTH ON CURVE SEGMENT

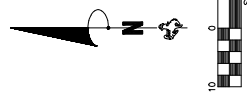

CURVE TABLE - BLOCK 7			
CURVE #	DELTA	CHORD LENGTH	ARC LENGTH
1	10° 00' 00"	10.000'	10.472'
2	20° 00' 00"	20.000'	20.944'
3	30° 00' 00"	30.000'	31.416'

CURVE TABLE - BLOCK 14			
CURVE #	DELTA	CHORD LENGTH	ARC LENGTH
1	10° 00' 00"	10.000'	10.472'
2	20° 00' 00"	20.000'	20.944'
3	30° 00' 00"	30.000'	31.416'

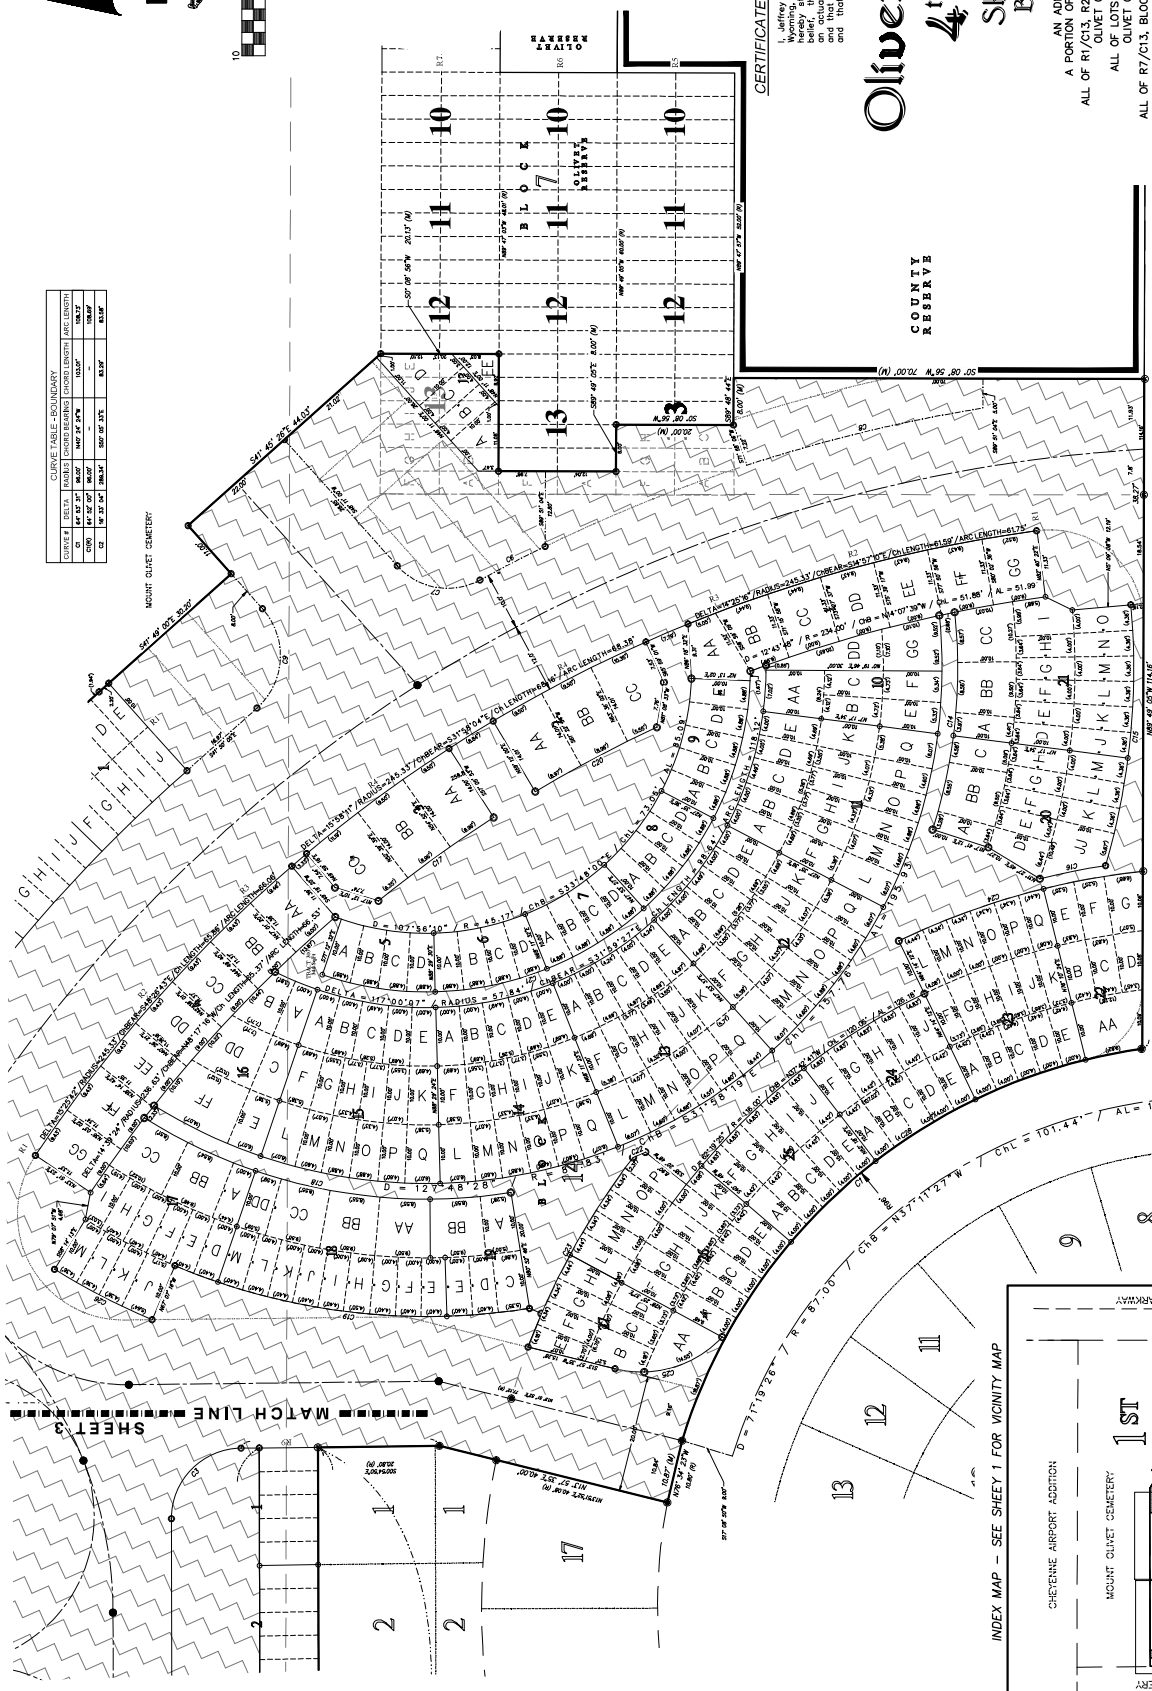

CERTIFICATE OF SURVEYOR

I, Jeffrey B. Jones, a Professional Land Surveyor in the State of Wyoming, for and on behalf of Steel Surveying Services, LLC, do hereby certify that this map was prepared from field notes taken during an actual survey made by me or under my direct supervision, and that the monuments found or set are as shown.

Olivet Cemetery

4th Filing

Sheet 2 of 5

Blocks 7 & 14


AN ADMINISTRATIVE REPORT OF
A PORTION OF THE SURFACE ESTATE OF
ALL OF R7/C13, R2/C13, R3/C13, & R4/C13, BLOCK 4,
OLIVET CEMETERY 3rd FILING AND
ALL OF LOTS A, B, & F, R5/C13, BLOCK 4,
OLIVET CEMETERY 3rd FILING AND
ALL OF R7/C13, BLOCK 4, OLIVET CEMETERY 3rd FILING AND
ALL OF BLOCK 7, INCLUSIVE, OLIVET CEMETERY; 3rd FILING
CITY OF CHEYENNE, LARAMIE COUNTY, WYOMING

PREPARED MAY 2019

STEEL SURVEYING SERVICES, LLC
PROFESSIONAL LAND SURVEYORS
PLANNING & DEVELOPMENT SPECIALISTS
1108 WEST 19th ST. CHEYENNE, WY. 82001 • (307) 634-7873
750 GILBERT ST. WHEATLAND, WY. 82201 • (307) 333-9789
www.steelsurvey.com • info@steelsurvey.com



INDEX MAP - SEE SHEET 1 FOR VICINITY MAP



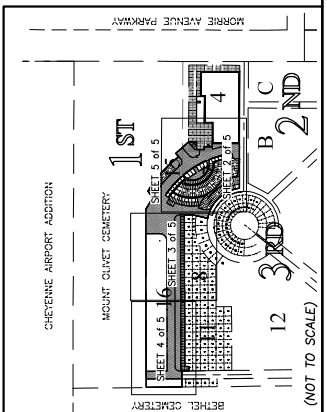


REVISION: 1/19/2022
Storage/2015/Drawings/2019 DWP/10086 OLIVET REPLAT/10086 Olivet4th_Filing-2022.dwg
© COPYRIGHT 2020 STEEL SURVEYING SERVICES, LLC. ALL RIGHTS RESERVED

CURVE TABLE - BOUNDARY					
CURVE #	DELTA	RADIUS	CHORD BEARING	CHORD LENGTH	ARC LENGTH
C1	64° 53' 31"	96.00'	N40° 24' 24"W	103.00'	108.73'
C10	64° 53' 00"	96.00'	—	—	108.68'
C2	140° 33' 04"	208.34'	S60° 00' 31"E	83.30'	83.86'

LEGEND

⊙	SET 1½" ALUMINUM CAP ON ¾"x24" REBAR STAMPED "SSS P.L.S. 5910"
●	FOUND 1½" ALUMINUM CAP STAMPED

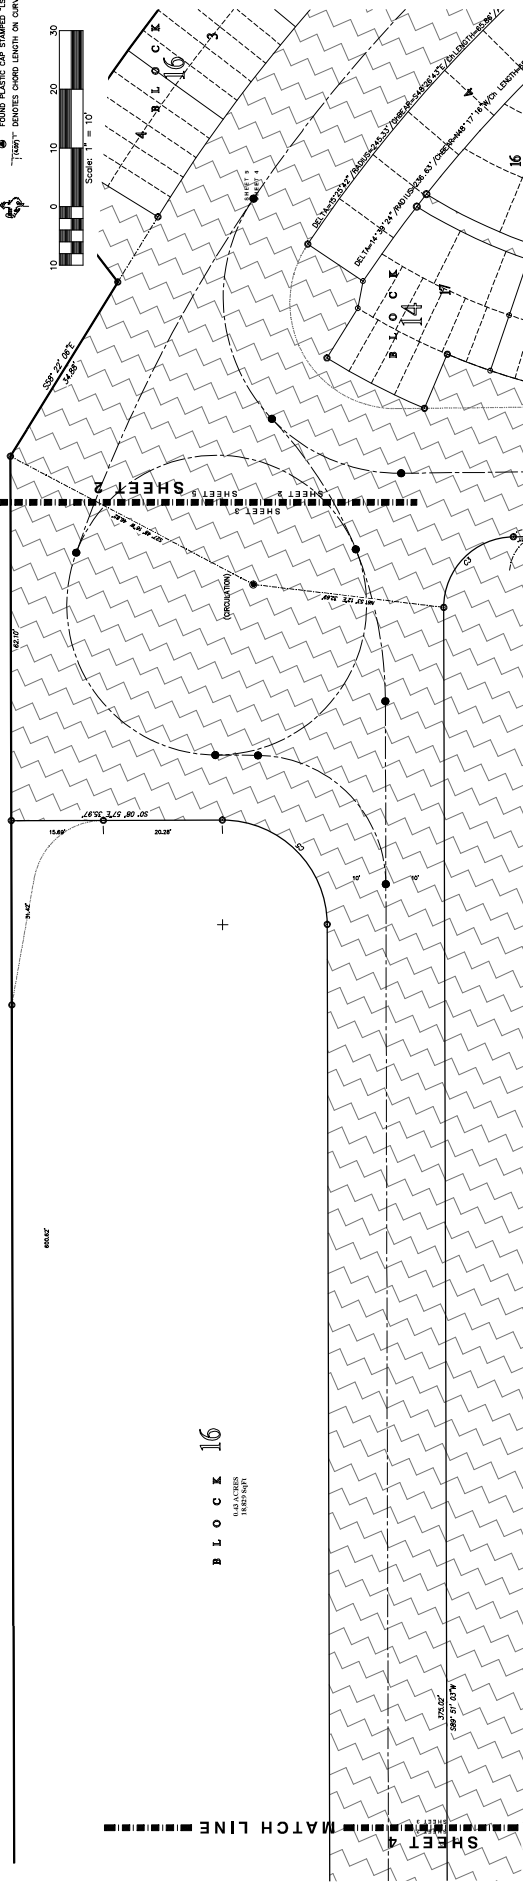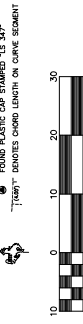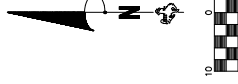


CURVE TABLE - BLOCKS 8 & 11					
CURVE #	DELTA	RADIUS	CHORD BEARING	CHORD LENGTH	ARC LENGTH
C3	89° 29' 50"	12.00'	N45° 23' 50"W	16.00'	18.74'
C4	88° 34' 00"	19.00'	S44° 37' 50"E	27.00'	18.94'

CURVE TABLE - BLOCKS 8 & 11					
CURVE #	DELTA	RADIUS	CHORD BEARING	CHORD LENGTH	ARC LENGTH
C3	89° 29' 50"	12.00'	N45° 23' 50"W	16.00'	18.76'
C4	88° 34' 00"	19.00'	S44° 37' 50"E	27.00'	18.94'

CERTIFICATE OF SURVEYOR

I, Jeffrey B. Jones, A Professional Land Surveyor in the State of Wyoming, for and on behalf of Stelli Surveying Services, LLC, hereby state, to the best of my knowledge, information and belief, that this map was prepared from field notes taken during an actual survey made by me or under my direct supervision; and that this map correctly shows the results of said survey.

Olivet Cemetery
4th Filing

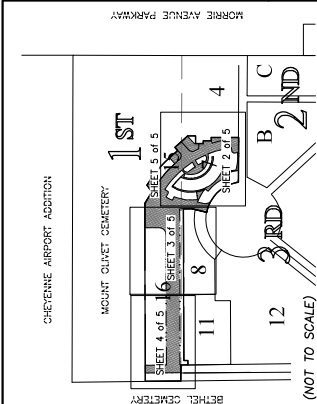

FILING RECORD

(NOT TO SCALE)

storage2015\DRAWINGS\2019 DWG\19086 OLIVET REPLAT\19086 Olivet4th_Rev2-2022.dwg
© COPYRIGHT 2020 STER SURVEYING SERVICES, LLC. ALL RIGHTS RESERVED
REVISED: 1/27/2021

REVISED: 1/27/2021
\\2019 DWG\19086 OLIVET REPLAT\19086 Olivet4th_Rev2--2022.dwg
©COPYRIGHT 2020 STEEL SUBMITTING SERVICES LLC ALL RIGHTS RESERVED



PREPARED MAY 2019

STEIL SURVEYING SERVICES, LLC
PROFESSIONAL LAND SURVEYORS
PLANNING & DEVELOPMENT SPECIALISTS
 1108 WEST 10th ST. CHEYENNE, WY. 82001 • (307) 654-7273
 756 GILCHRIST ST. WHEATLAND, WY. 82201 • (307) 328-8766
www.SteilSurvey.com • info@SteilSurvey.com

- DOMESTIC WATER & SANITARY SEWER PROVIDED BY CITY OF CHEYENNE BOPU - FIRE PROTECTION TO BE PROVIDED BY CHEYENNE FIRE & RESCUE - THE SURFACE ESTATE OF THE LAND TO BE SUBDIVIDED IS SUBJECT TO FULL AND EFFECTIVE DEVELOPMENT OF THE MINERAL ESTATE -




LEGEND

- 1" ALUMINUM CAP ON N-24° REBAR STAMPED 2008 P.L.S. 59107
- FOUND 1 1/2" ALUMINUM CAP STAMPED 2008 P.L.S. 59107
- FOUND 1" REBAR
- FOUND 1 1/2" REBAR
- FOUND 1 1/2" R/W MONUMENT
- FOUND CHISELED "X"
- FOUND PLASTIC CAP STAMPED "LS 347"
- 1/4" REBAR CHORD LENGTH ON CURVE SEGMENT

Scale: 1" = 10'



INDEX MAP - SEE SHEET 1 FOR VICINITY MAP

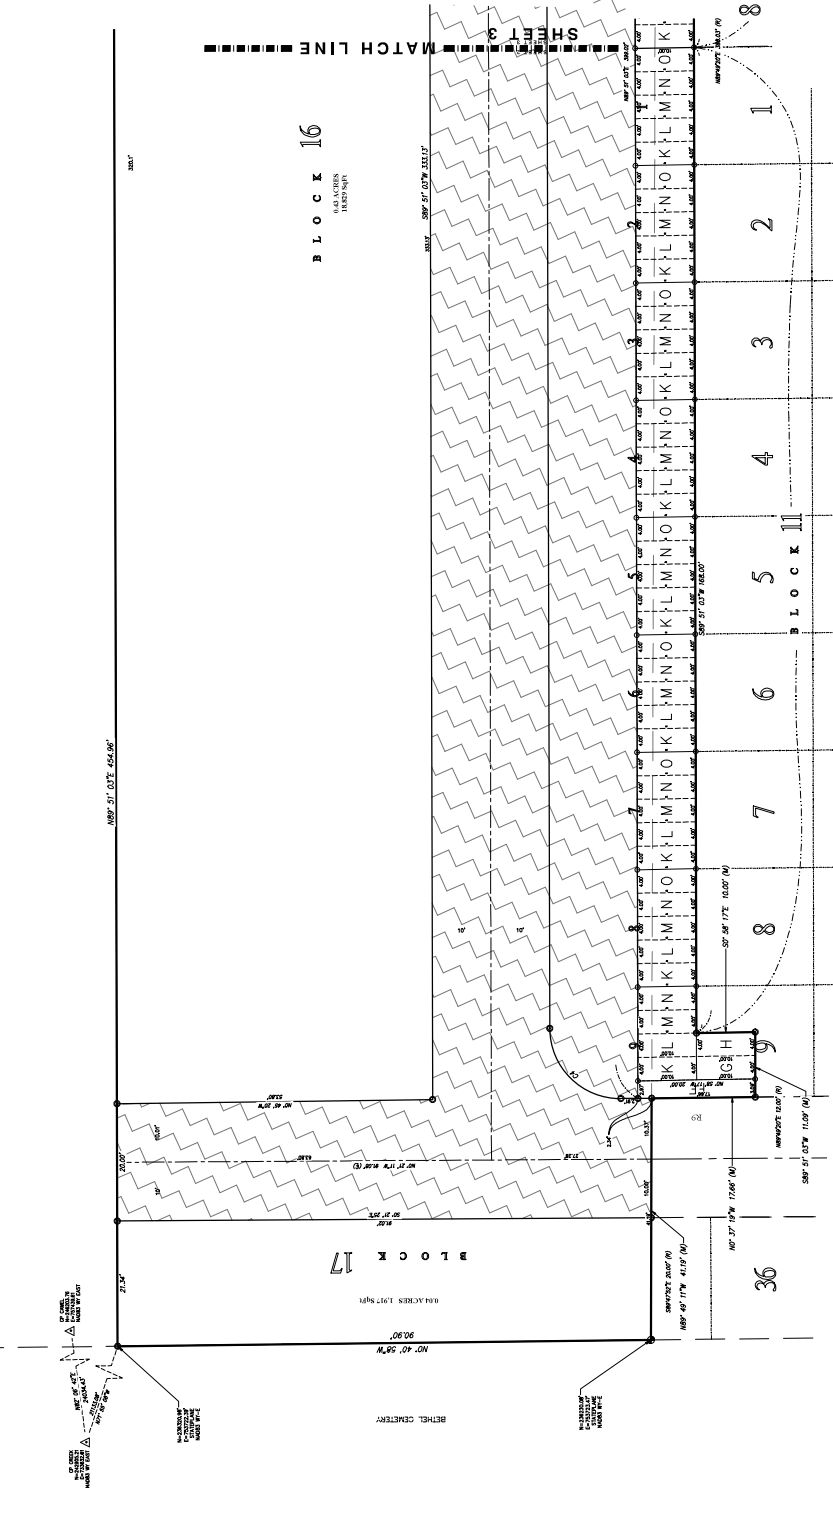

CURVE TABLE - BLOCKS 16 & 17			
STATION	CHORD BEARING	CHORD LENGTH	ARC LENGTH
10+00	S 89° 56' 48" W	10.00'	10.00'
11+00	S 89° 56' 48" W	10.00'	10.00'
CERTIFICATE OF SURVEYOR

I, Jeffrey B. Jones, a Professional Land Surveyor in the State of Wyoming, for and on behalf of Steel Surveying Services, LLC, Wyoming, do hereby certify that the foregoing is a true and correct copy of the original survey made by me or under my direct supervision, and that the monuments found or set are as shown.

Olivet Cemetery

4th Filing

Sheet 4 of 5


Blocks 11, 16 & 17

AN ADMINISTRATIVE REPEAT OF AN OLIVET CEMETERY AND A PORTION OF BLOCK 16, OLIVET CEMETERY AND ALL OF R7/C13, R2/C13, R3/C13, & R4/C13, BLOCK 4, OLIVET CEMETERY 3rd FILING AND ALL OF LOTS A, B, & F, R5/C13, BLOCK 4, OLIVET CEMETERY 3rd FILING AND ALL OF R7/C13, BLOCK 4, OLIVET CEMETERY 3rd FILING AND ALL OF BLOCK 7, INCLUSIVE, OLIVET CEMETERY; 3rd FILING CITY OF CHEYENNE, LARAMIE COUNTY, WYOMING

PREPARED MAY 2019




STEEL SURVEYING SERVICES, LLC
PROFESSIONAL LAND SURVEYORS
PLANNING & DEVELOPMENT SPECIALISTS
1108 WEST 19th ST. CHEYENNE, WY. 82001 • (307) 634-7879
750 GLOUCESTER ST. WHEATLAND, WY. 83091 • (307) 388-9789
www.steelsurvey.com • info@steelsurvey.com

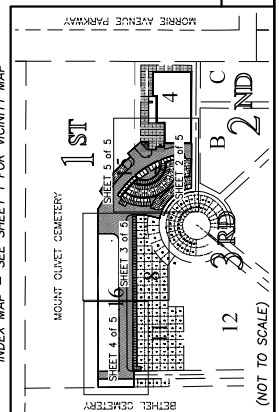

storage2015\DRAWINGS\2019 DMS\19086 OLIVET REPEAT\19086 OlivetRepl.dwg
REVISED: 1/27/2021
© COPYRIGHT 2020 STEEL SURVEYING SERVICES, LLC ALL RIGHTS RESERVED

- ① SET 1½" ALUMINUM CAP ON "24" REBAR
 STAMPED "SSS P.L.S. 5910"
 ② FOUND 1½" ALUMINUM CAP STAMPED
 "SSS P.L.S. 2500"
 ③ FOUND ¾" REBAR
 ④ FOUND M.D.O.T. R/W MONUMENT
 ⑤ FOUND CHISELED "X"
 ⑥ FOUND PLASTIC CAP STAMPED "LS 347"
 ⑦ 1/168" DENOTES CHORD LENGTH ON CURVE SEGMENT

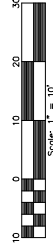

CURVE TABLE - BOUNDARY					
CURVE #	DELTA	RADIUS	CHORD BEARING	CHORD LENGTH	ARC LENGTH
C1	64° 53' 30"	94.00'	N40° 24' 24"W	103.00'	106.33'
C140	64° 52' 00"	94.00'	-	-	106.69'
C2	74° 33' 04"	209.34'	S60° 05' 33"E	84.29'	84.90'

CURVE TABLE - BLOCK 15					
CURVE #	DELTA	RADIUS	CHORD BEARING	CHORD LENGTH	ARC LENGTH
C10	P 45° 00"	548.35'	S 34° 14' 00" E	30.13'	30.16'

I, Jeffrey B. Jones, A Professional Land Surveyor in the State of Wyoming, for and on behalf of Stettin Surveying Services, LLC, hereby state, to the best of my knowledge, information and belief, that this map was prepared from field notes taken during an actual survey made by me or under my direct supervision; and that this map correctly shows the results of said survey and that the monuments found or set are as shown.

Olivet Cemetery
 4th Filing
 Sheet 5 of 5
 Block 15


AN ADMINISTRATIVE REPLAT OF
A PORTION OF MOUNT OLIVET CEMETERY AND
ALL OF R7/C13, R2/C13, R3/C13, & R4/C13; BLOCK 4,
OLIVET CEMETERY 3rd FILING AND
ALL OF LOTS A, B, & F, R5/C13, BLOCK 4,
OLIVET CEMETERY 3rd FILING AND
ALL OF R7/C13, BLOCK 4, OLIVET CEMETERY 3rd FILING AND
ALL OF BLOCK 7, INCLUSIVE, OLIVET CEMETERY, 3rd FILING
CITY OF CHEYENNE, LARAMIE COUNTY, WYOMING

PREPARED MAY 2019

STEEL SURVEYING SERVICES, LLC
PROFESSIONAL LAND SURVEYORS
PLANNING & DEVELOPMENT SPECIALISTS
 1108 WEST 16th ST. CHRYSTENNE, WY. 83001 • (307) 634-7373
 756 GILCHRIST ST. WHEATLAND, WY. 83091 • (307) 328-8789
www.SteelSurvey.com • info@SteelSurvey.com



storage2015\DRAWINGS\2019 DWG\19086 OLIVET REPLAT\19086 Olivet4th_Rev2--2022.dwg
REVISED: 1/27/2021
© COPYRIGHT 2020 STEEL SURVEYING SERVICES, LLC ALL RIGHTS RESERVED

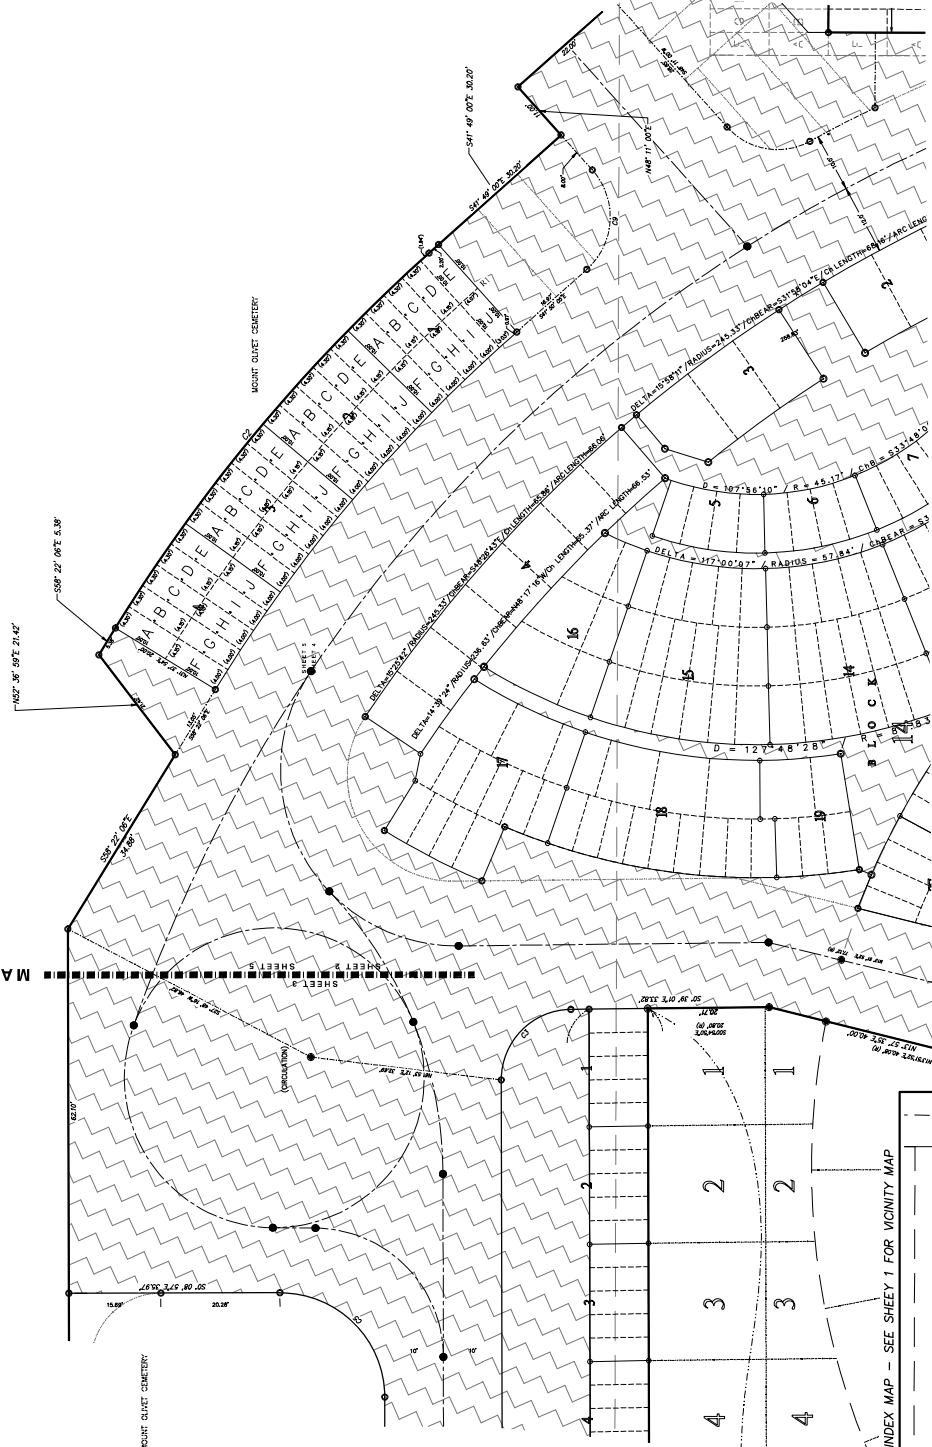

INDEX MAP - SEE SHEET 1 FOR VICINITY MAP

MOUNT OLIVET CEMETERY

MORRIS AVENUE PARKWAY

FILING RECORD

(NOT TO SCALE)

$$\frac{Z}{Z'}$$